




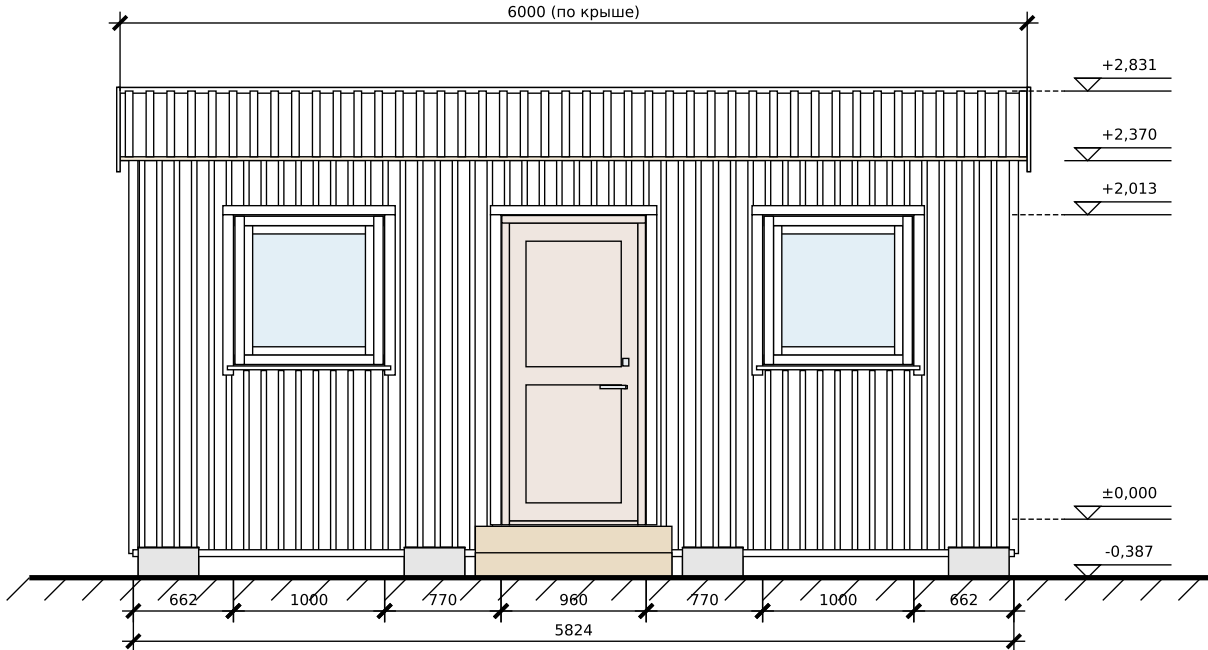


Главный фасад М 1:50

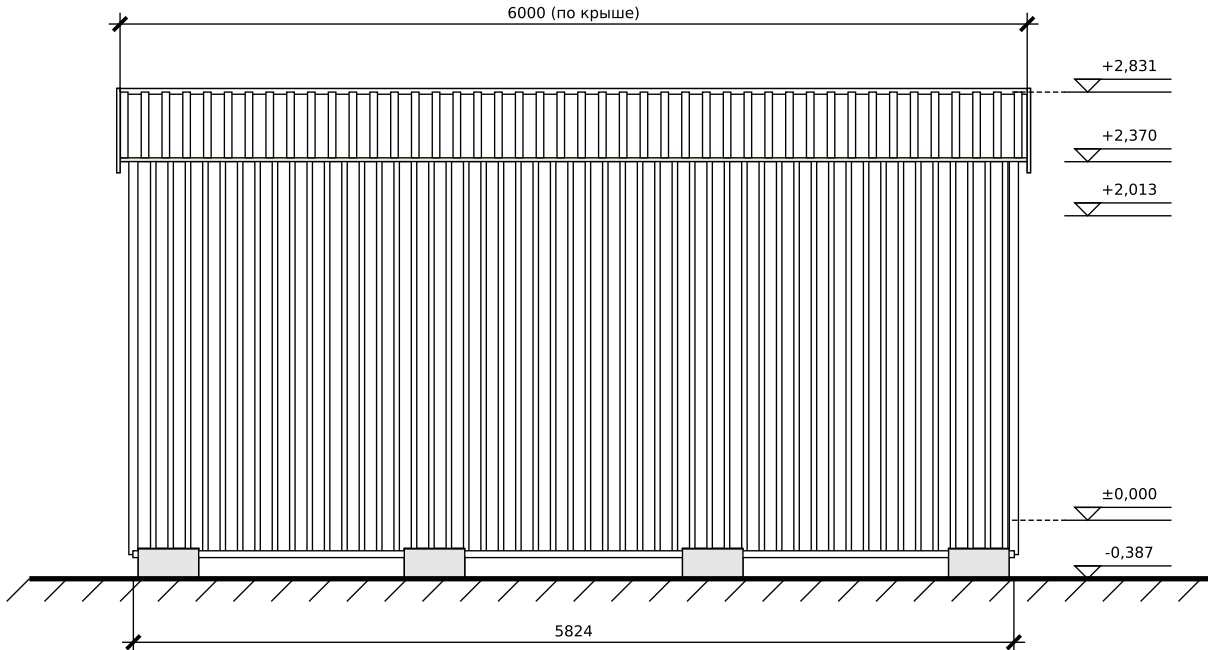

Задний фасад М 1:50

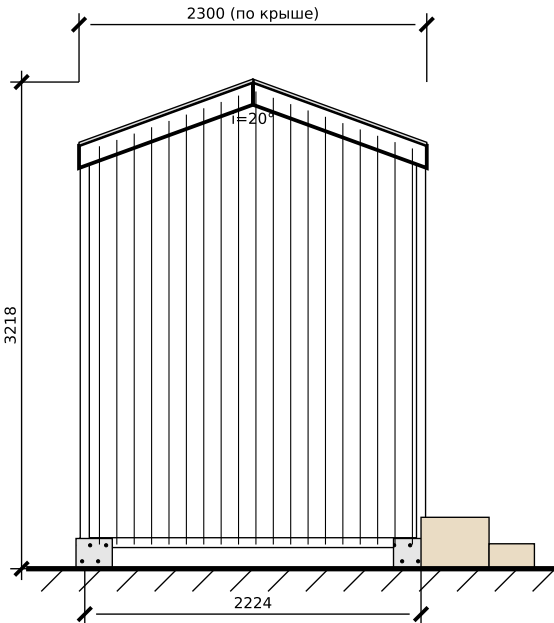

Левый торец М 1:50

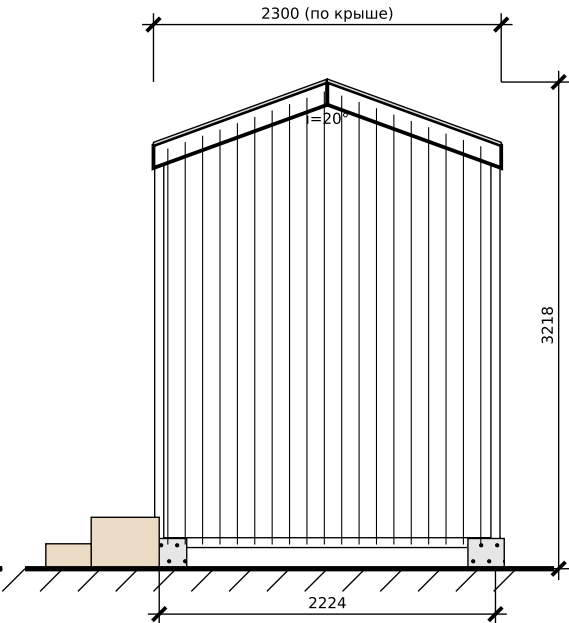


Правый торец М 1:50

Ведомость отделки фасадов

Элемент	Материал	Цвет
Стены	Профлист С8-1150, 0,45 мм, полимер	RAL 6005*
Нащельники, углы, наличники, отливы	Доборные элементы, полимер	RAL 9003
Кровля	Профлист С20-1100, 0,45 мм, оцинк.	металлик
Конёк, ветр. планки	Оцинкованная сталь / полимер	по кровле
Окна	ПВХ, 2-кам. стеклопакет	белые
Дверь	Металлическая, пр-во РФ	RAL 8017
Ступени	Доска 40 мм, антисептик	тик/орех


* Цвет стен — по выбору заказчика. Варианты визуализации:
RAL 6005 зелёный мох · RAL 8017 шоколад · RAL 5005 синий ·
RAL 3005 вишня · RAL 1015 слоновая кость (images/color_*.png).
Отметка ±0,000 — уровень чистого пола.

						ХБ-6.0х2.3-АР			
						Хозблок 6,0 × 2,3 м (по крыше) каркасный, утеплённый, с наполнением для хранения	Стадия	Лист	Листов
							Р	1	6
Изм.	Кор.уч	Лист	№ док.	Подп.	Дата		Частный заказ М 1:50		
Разраб.			Claude						
Пров.						Фасады. Цветовое решение	Размеры — мм, отметки — м		
Т.контр.									
Н.контр.									
Утв.					09.2026				

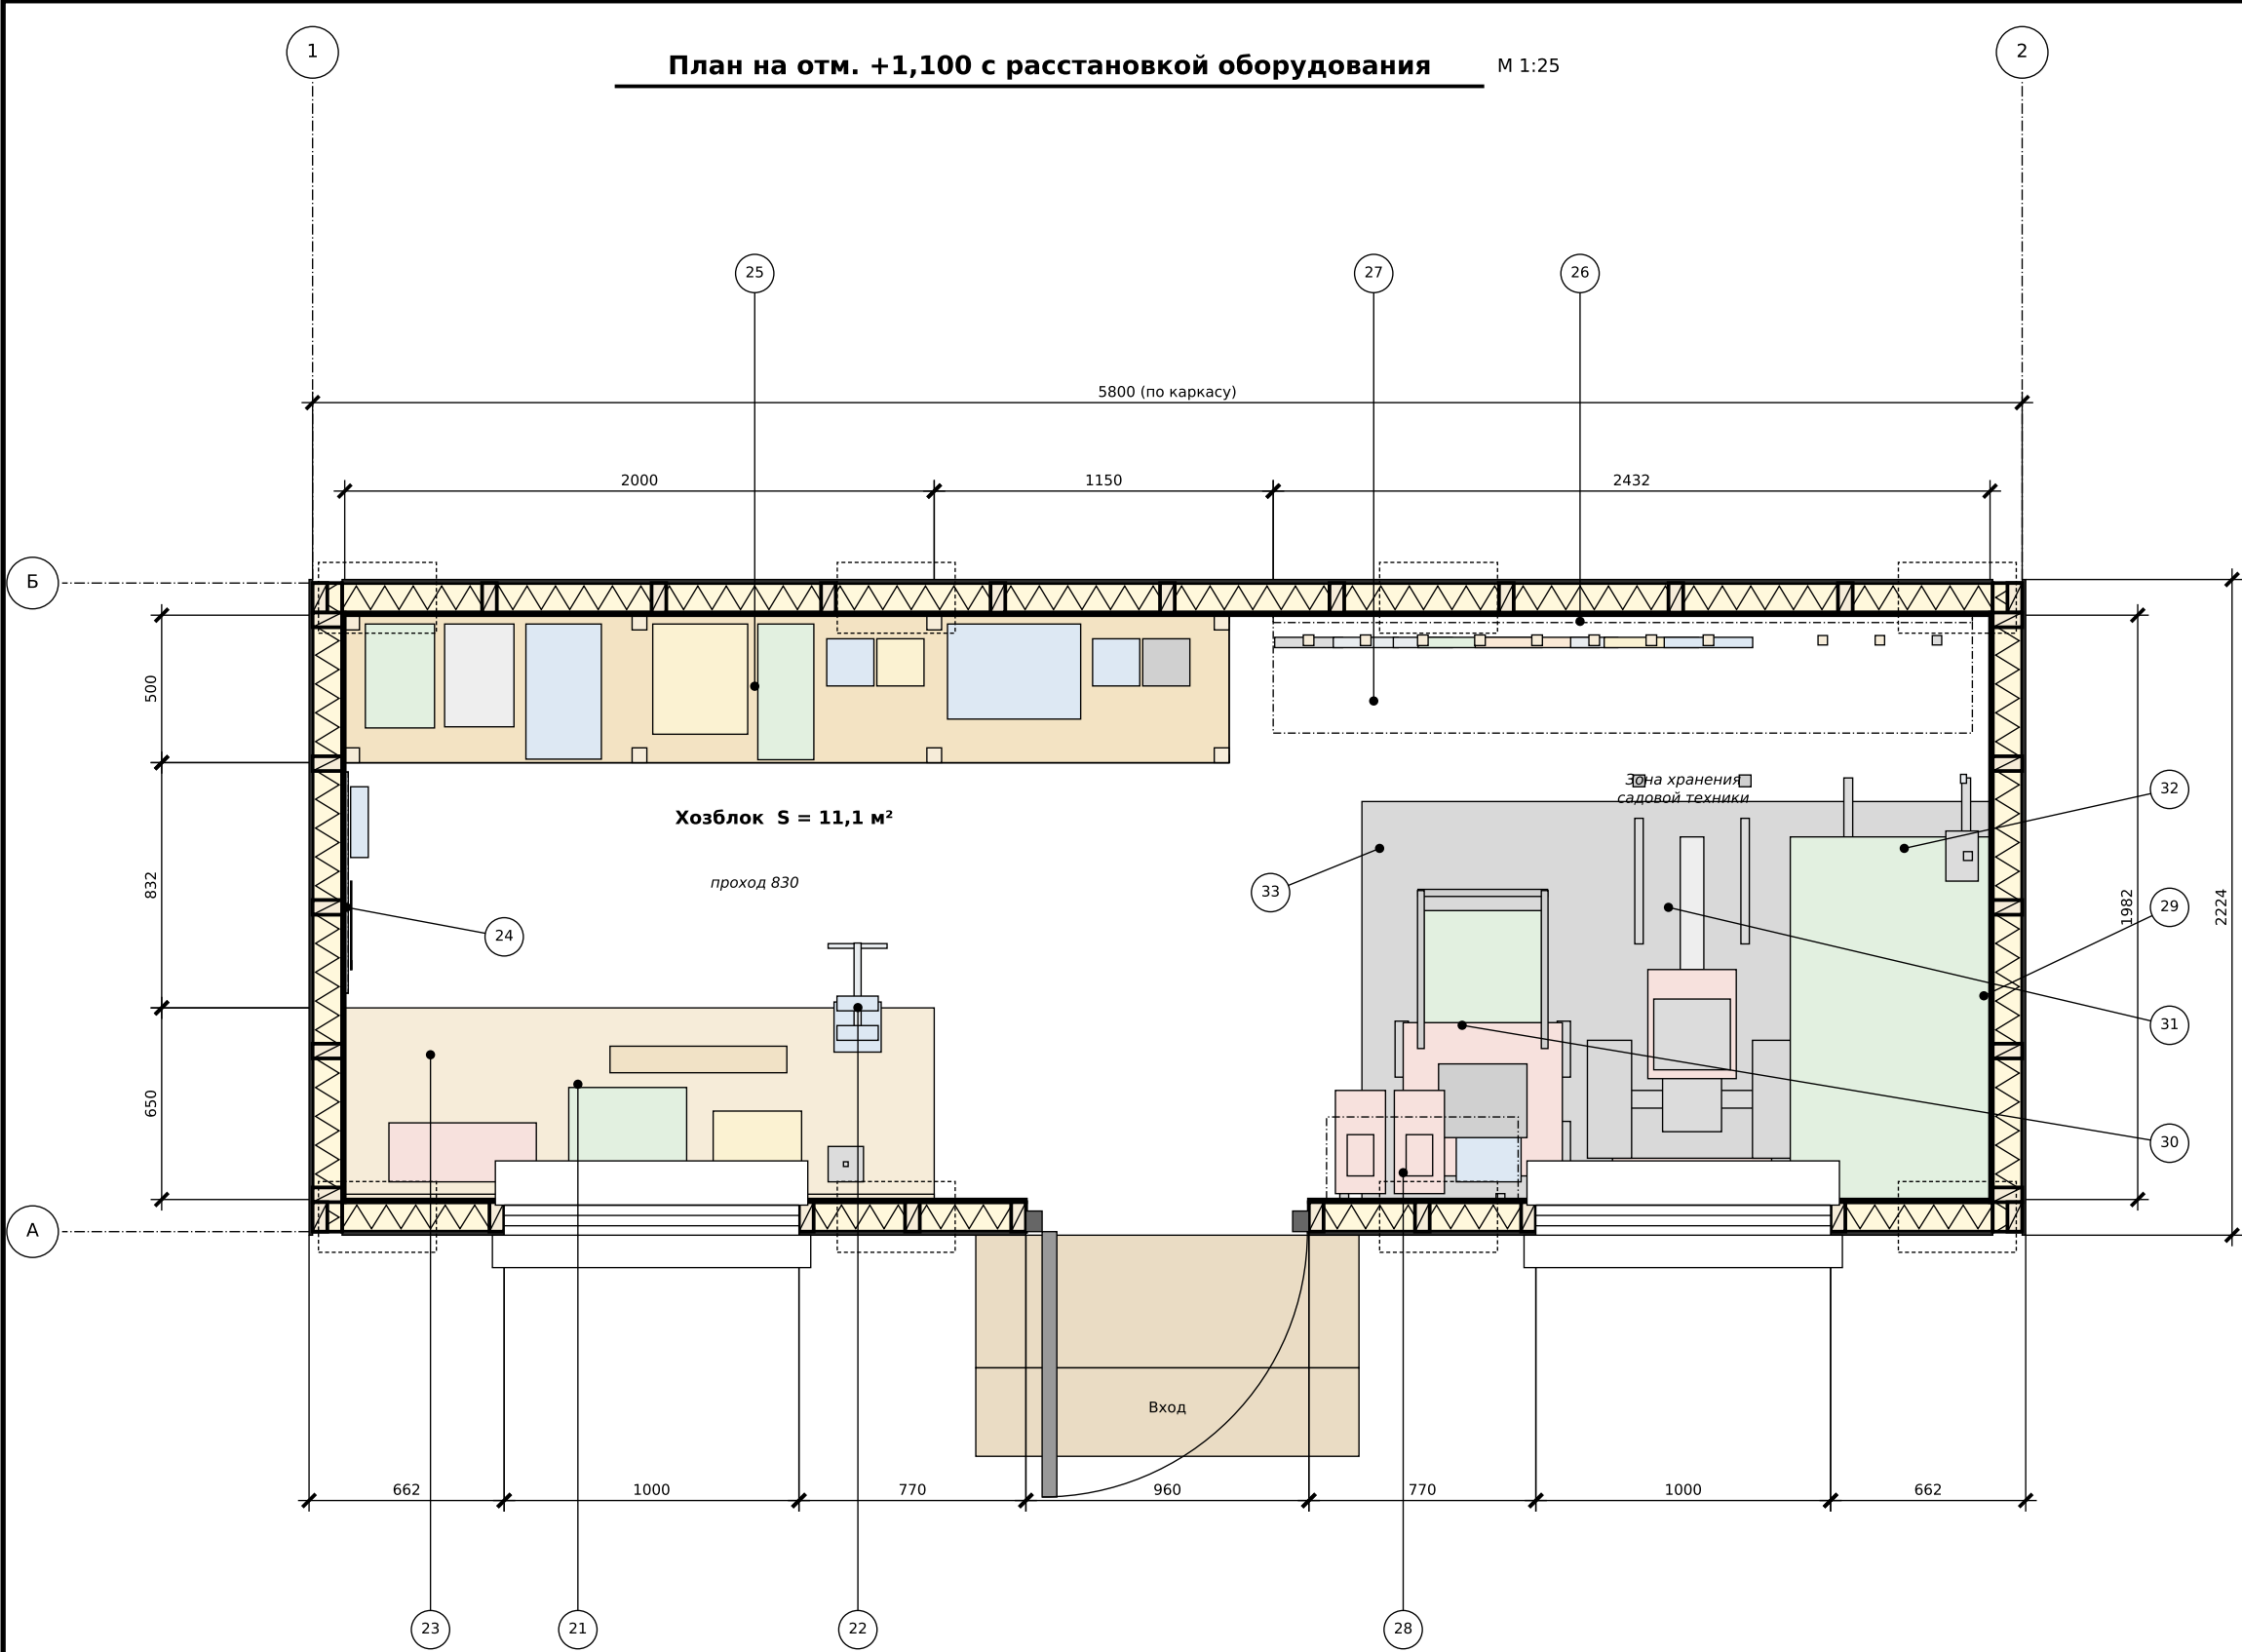

Экспликация оборудования		
Поз.	Наименование	Кол.
21	Верстак 2000×650, h=900	1
22	Тиски слесарные 125 мм	1
23	Тумба-кассетница под верстак	1
24	Перфопанель 750×1000	1
25	Стеллаж 3000×500×2100, 5 ярусов	1
26	Инструментальная стена	1
27	Антресоль 2430×400 на кронштейнах	1
28	Полки для ГСМ/мелочей 690×280	2
29	Рейка с крюками (шланг, удлинитель, триммер)	1
30	Место газонокосилки	—
31	Место мотоблока / культиватора	—
32	Место садовой тачки	—
33	Коврик резиновый под технику	1
34	Светильник LED 1200 мм (опция)	2


Материалы наполнения — лист 6.

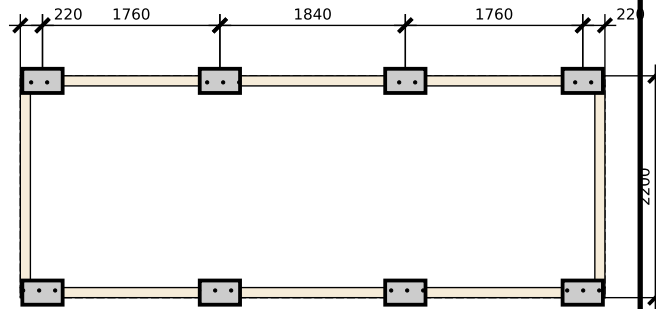

План фундамента М 1:75


Опоры — блоки бетонные 400×200×200 (8 шт.)
на песчано-щебёночной подушке 100 мм,
гидроизоляция — рубероид в 2 слоя.
Горизонтальность обвязки выставить
подкладками из рубероида/пластин ±5 мм.

						ХБ-6.0х2.3-АР			
						Хозблок 6,0 × 2,3 м (по крыше) каркасный, утеплённый, с наполнением для хранения	Стадия	Лист	Листов
							Р	2	6
							Частный заказ М 1:25, 1:75		
Изм. Кор.уч Лист	№док.	Подп.	Дата						
Разраб.	Claude								
Пров.						План с расстановкой оборудования. План фундамента			
Т.контр.									
Н.контр.									
Утв.			09.2026						

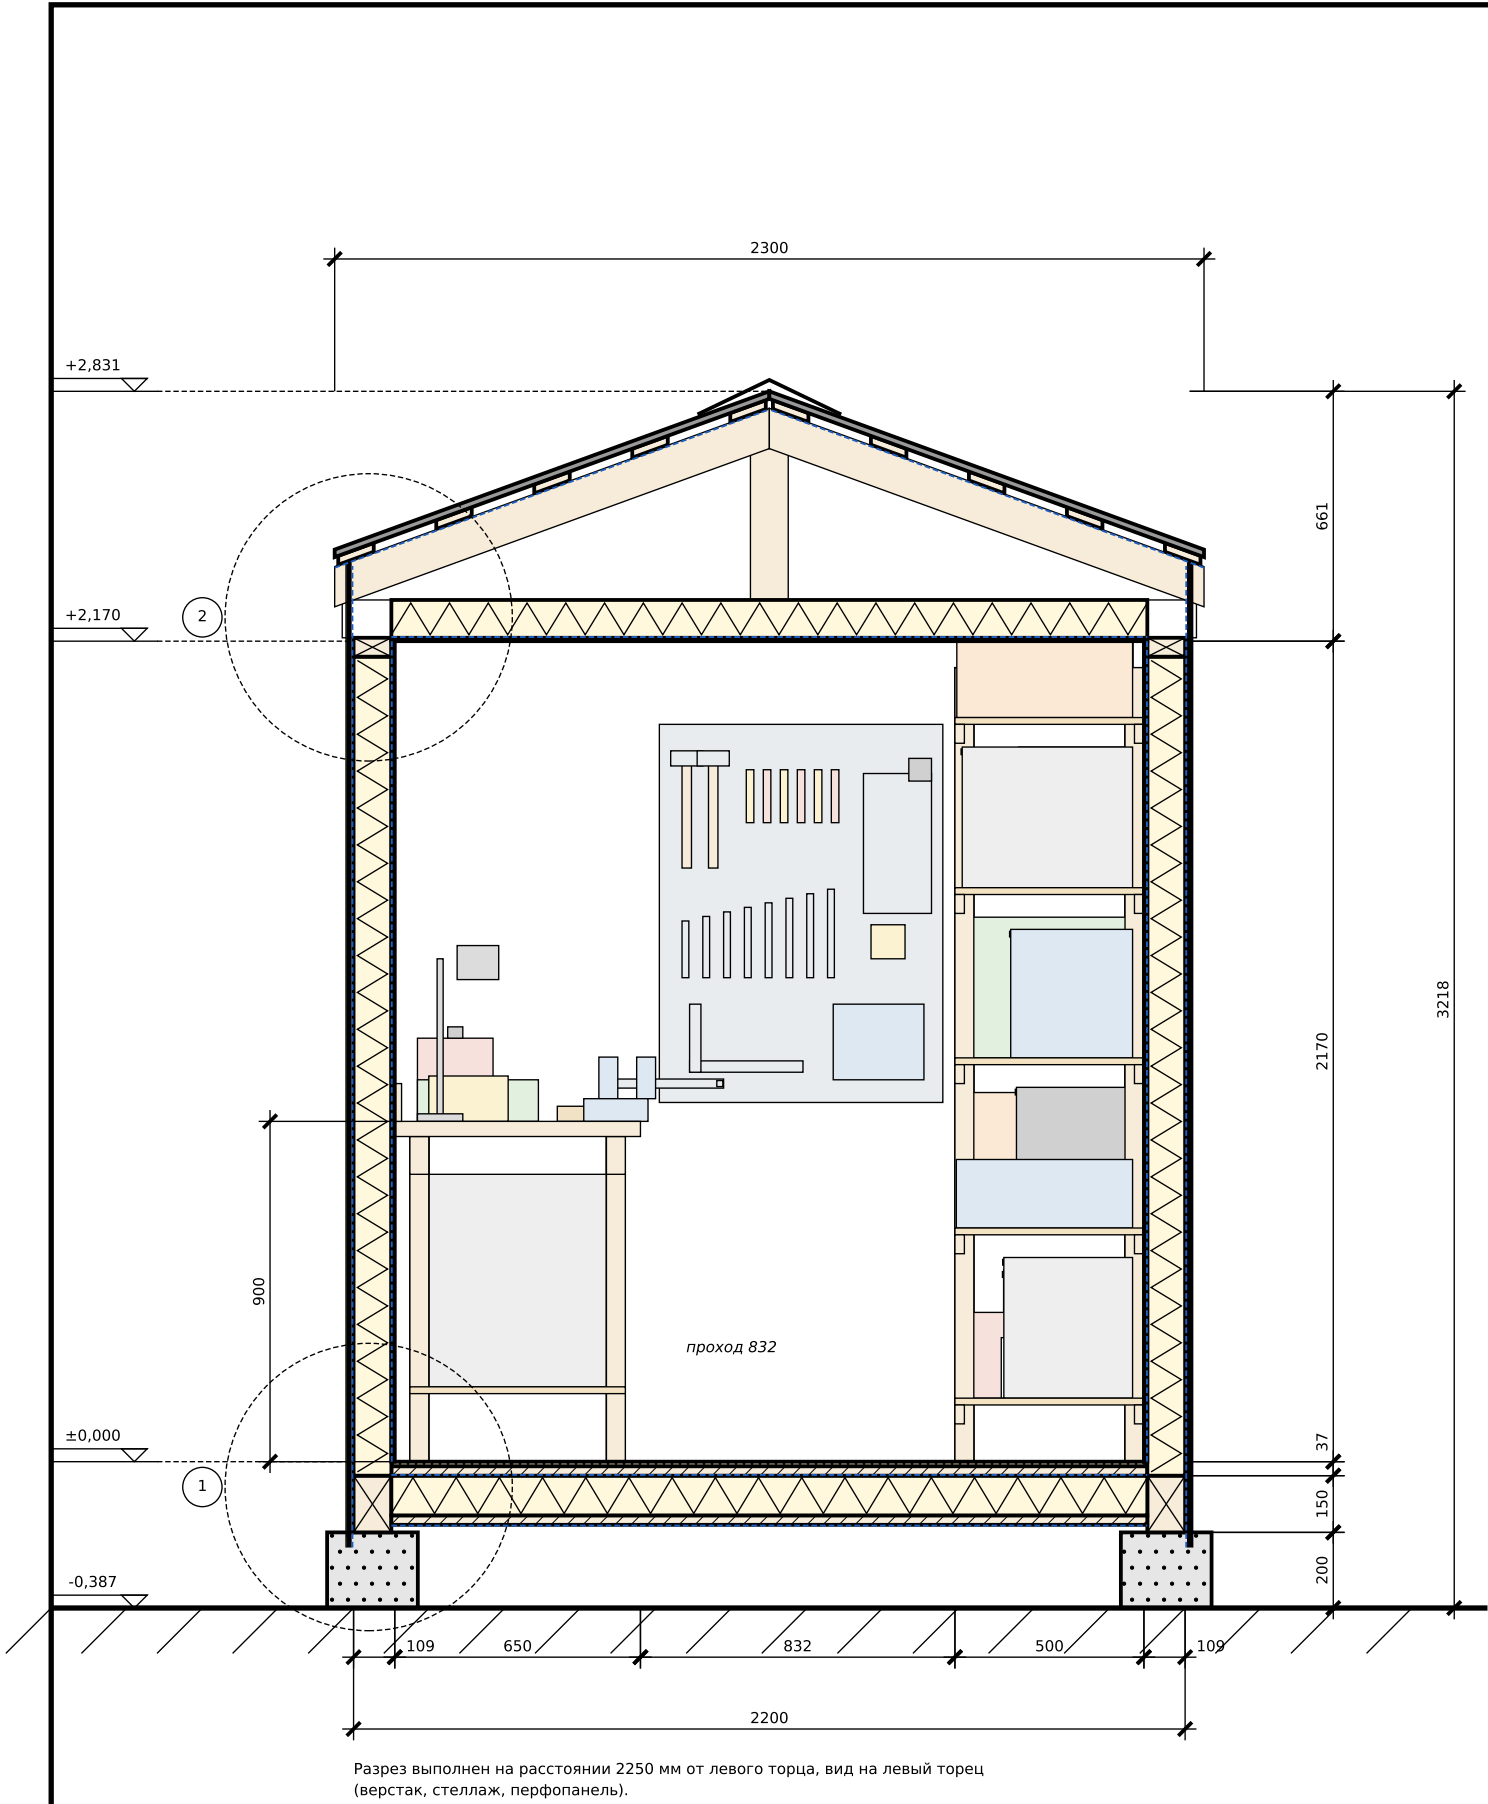


Разрез выполнен на расстоянии 2250 мм от левого торца, вид на левый торец (верстак, стеллаж, перфопанель).

Разрез 1-1 М 1:20

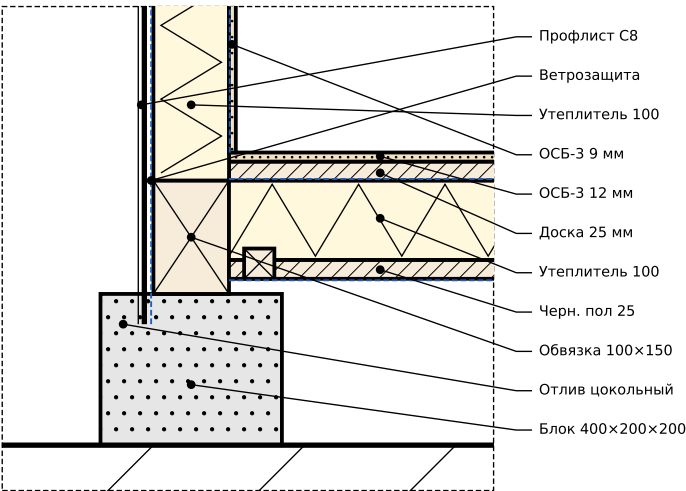

Узел 1 М 1:10

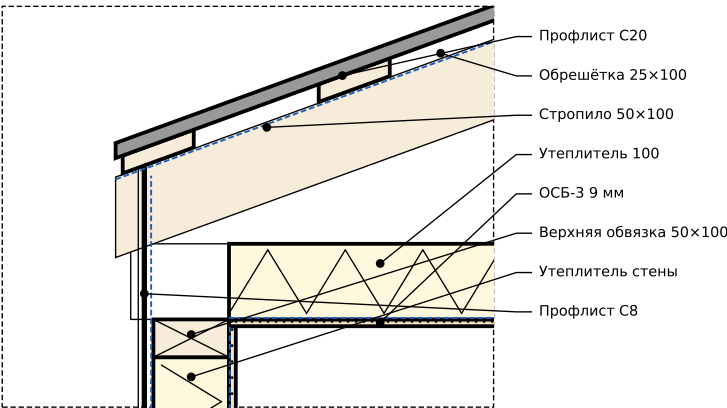

Узел 2 М 1:10

Состав конструкций (снаружи внутри)

Кровля:

1. Профлист С20 оцинкованный 0,45 мм
2. Обрешётка доска 25×100, шаг 300
3. Гидроизоляция (Изоспан D)
4. Стропила 50×100, шаг 575 (фермы)

Потолок:

1. Нижний пояс фермы 50×100
2. Утеплитель мин. вата 100 мм
3. Пароизоляция (Изоспан В)
4. ОСБ-3 9 мм

Стена:


1. Профлист С8 0,45 мм, полимер
2. Ветро-влагозащита (Изоспан А)
3. Каркас 50×100, шаг ≤600 + утеплитель 100
4. Пароизоляция (Изоспан В)
5. ОСБ-3 9 мм

Пол:


1. ОСБ-3 12 мм
2. Доска обрешечная 25 мм
3. Пароизоляция (Изоспан В)
4. Утеплитель мин. вата 100 мм между лагами 50×150
5. Ветро-влагозащита (Изоспан А)
6. Черновой пол доска 25 мм на черепном бруске 40×40

- Примечания:
1. Высота помещения в чистоте 2170 мм — под металлическую дверь 2050×960.
 2. Пароизоляцию укладывать с нахлёстом 100 мм, стыки проклеить соединительной лентой.
 3. Пиломатериал — хвойных пород, 1-2 сорт, обработать антисептиком.
 4. Утеплитель — минвата плотн. ≥ 35 кг/м³.


						ХБ-6.0х2.3-АР			
						Хозблок 6,0 × 2,3 м (по крыше) каркасный, утеплённый, с наполнением для хранения	Стадия	Лист	Листов
							Р	3	6
							Частный заказ М 1:20, 1:10		
Изм.	Кол.уч	Лист	№док.	Подп.	Дата	Разрез 1-1. Узлы 1, 2. Состав конструкций	Размеры — мм, отметки — м		
Разраб.		Claude							
Пров.									
Т.контр.									
Н.контр.									
Утв.			09.2026						

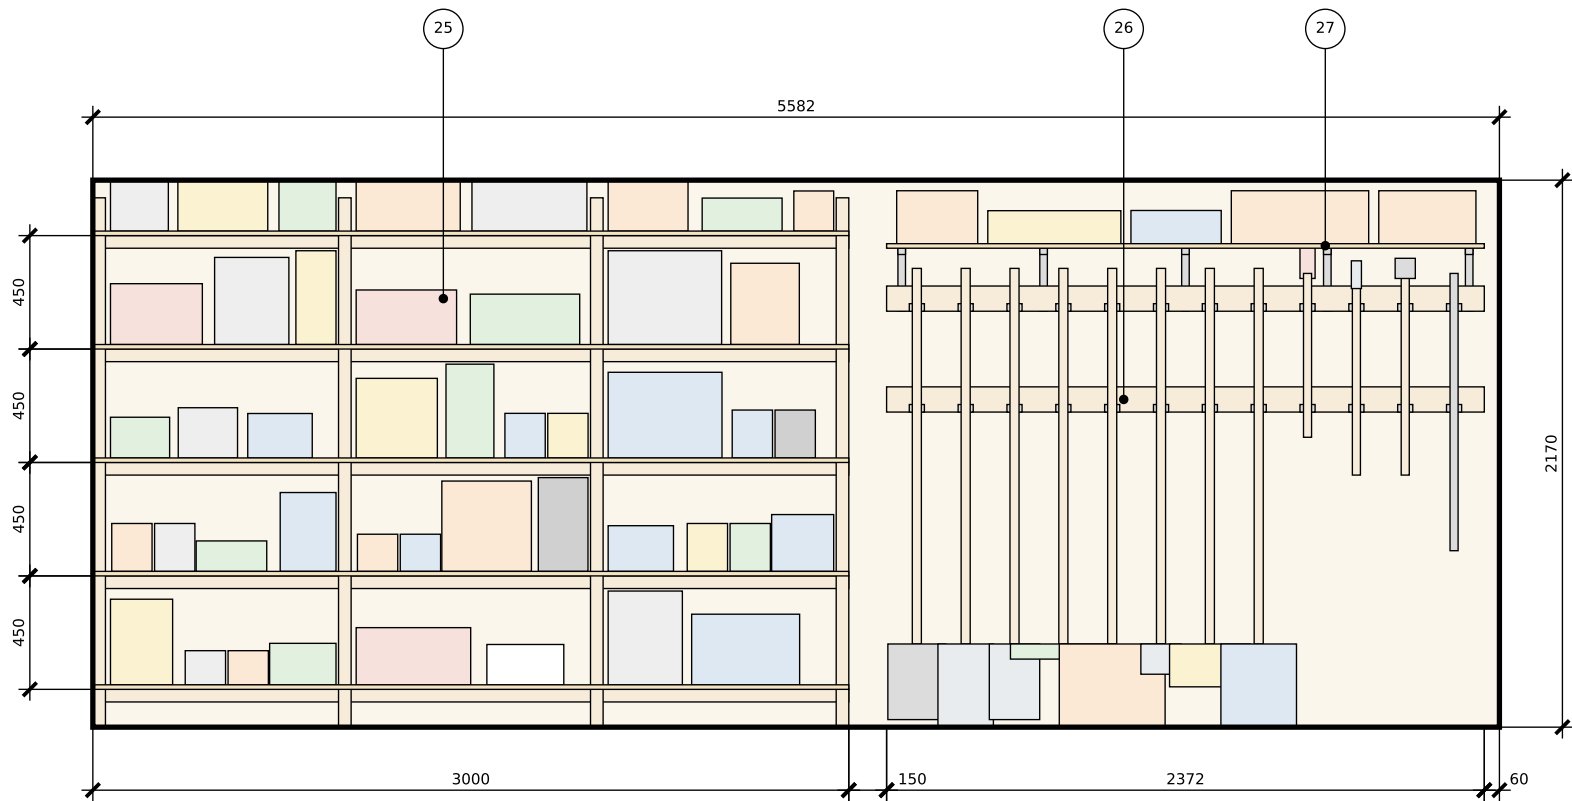


Развёртка А — задняя стена М 1:30

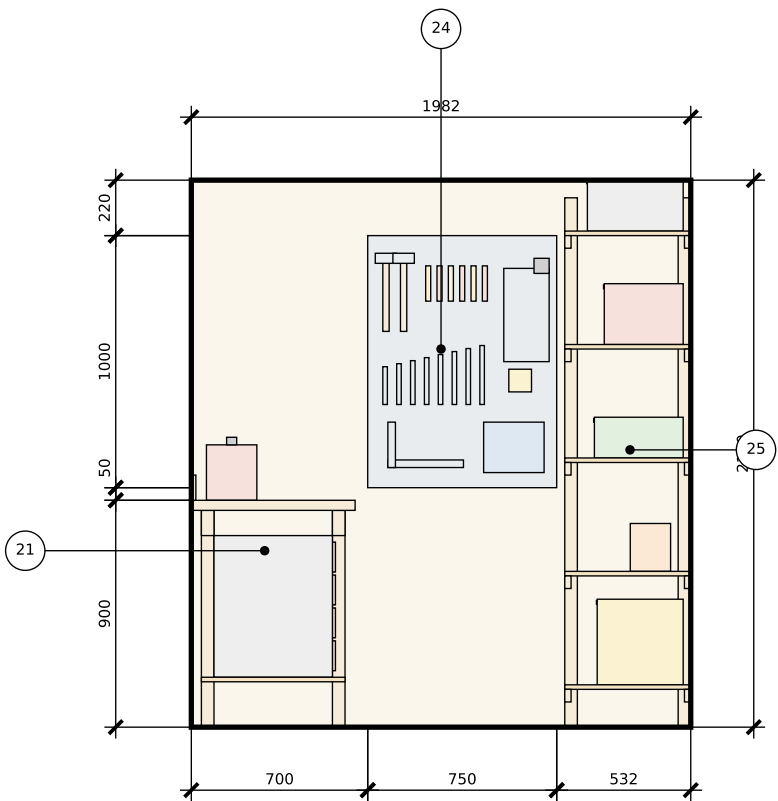

Развёртка В — левый торец М 1:30

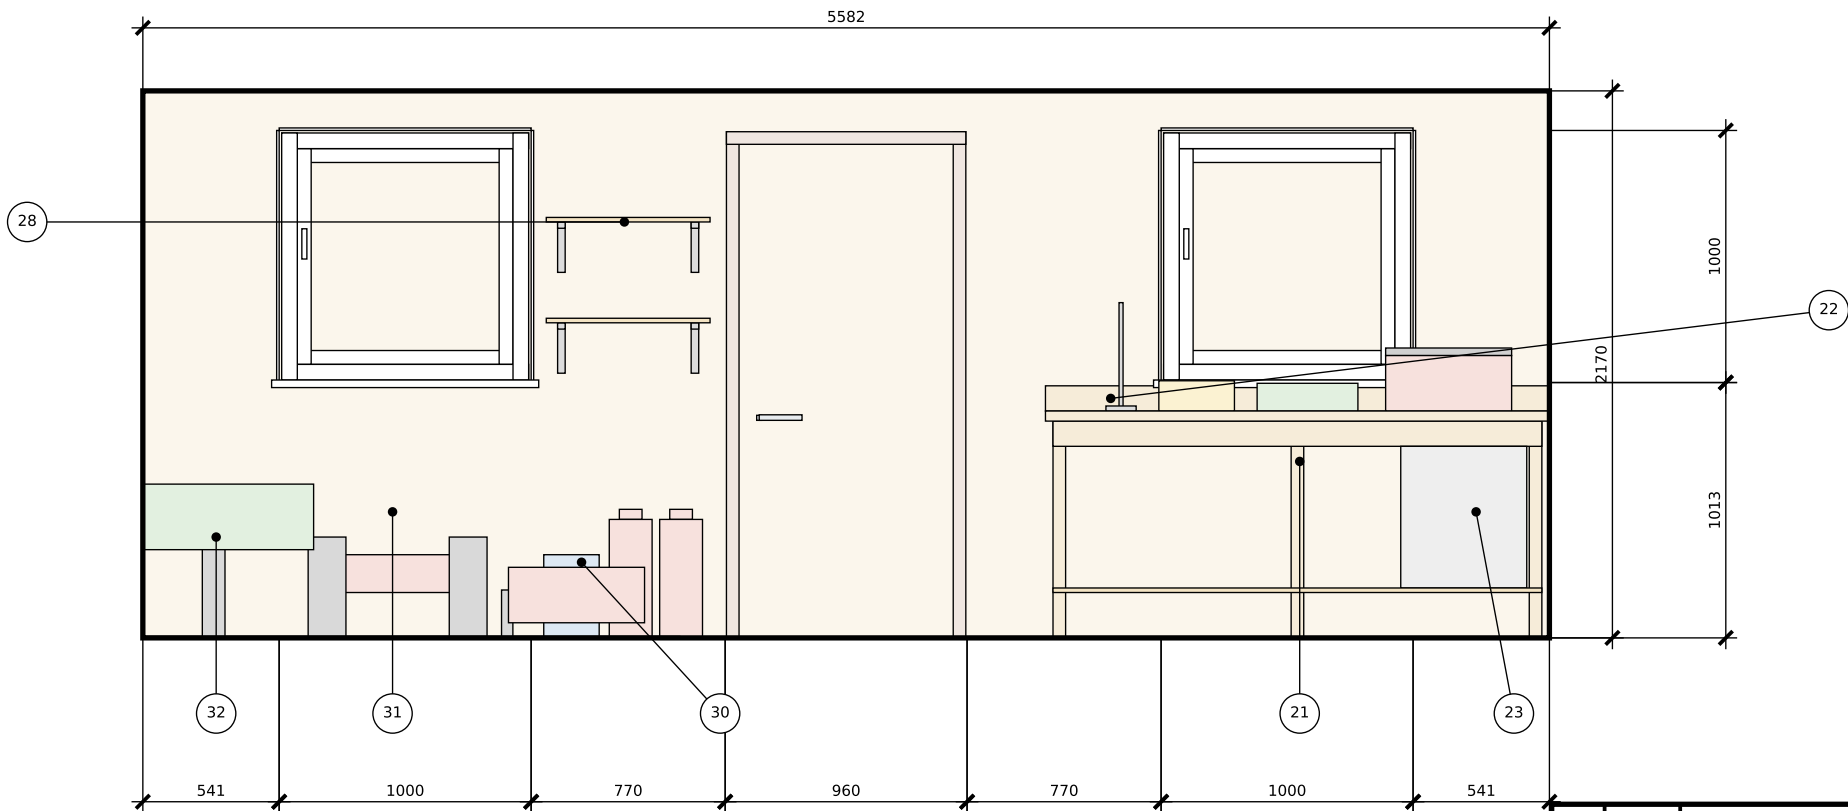


Развёртка Б — стена с дверью и окнами М 1:30

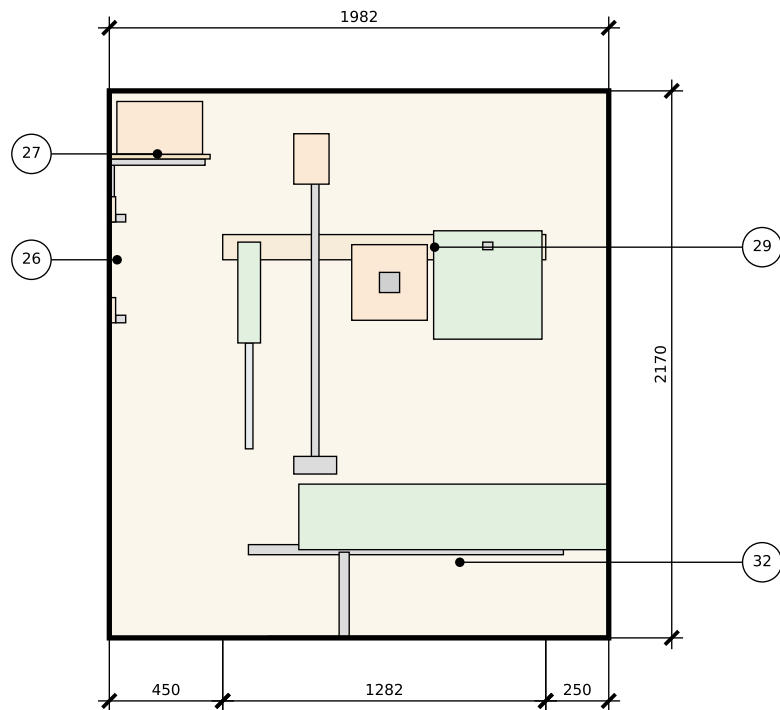


Развёртка Г — правый торец М 1:30


						ХБ-6.0x2.3-AP			
						Хозблок 6,0 × 2,3 м (по крыше) каркасный, утеплённый, с наполнением для хранения	Стадия	Лист	Листов
Изм.	Кор.уч	Лист	№ док.	Подп.	Дата		Р	4	6
Разраб.			Claude				Частный заказ		
Пров.									
Т.контр.						М 1:30			
						Развёртки внутренних стен с оборудованием	Размеры — мм, отметки — м		
Н.контр.									
Утв.					09.2026				

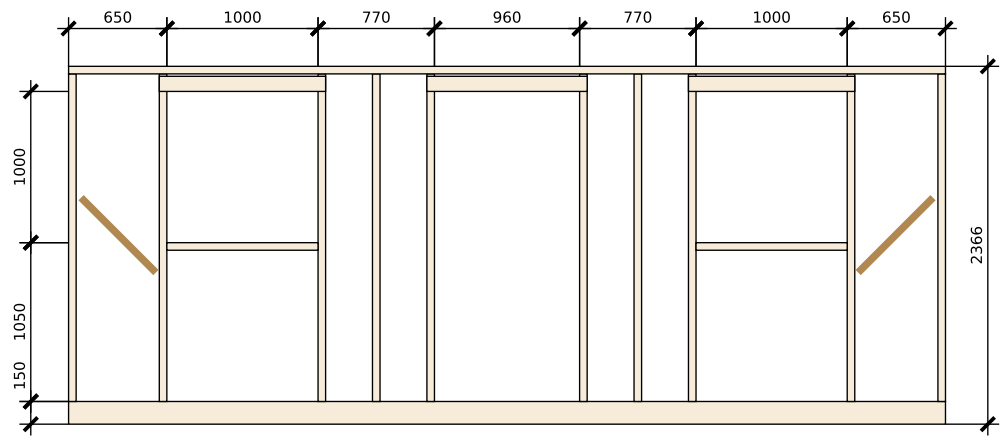

Стена по оси А (с проёмами) М 1:50

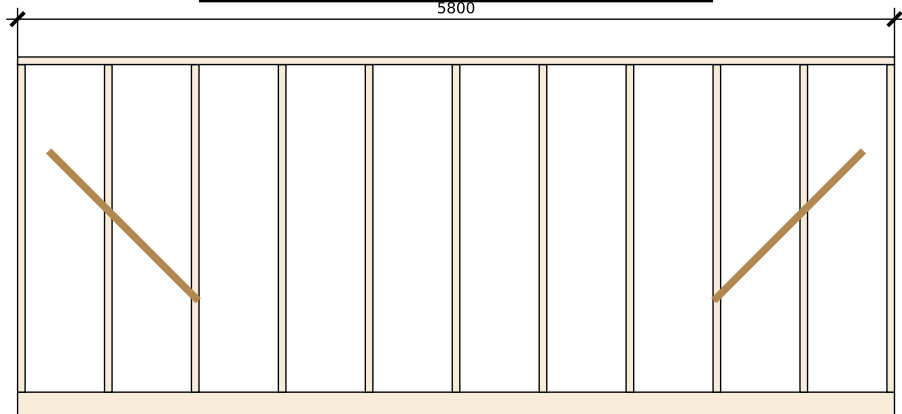


Стена по оси Б М 1:50

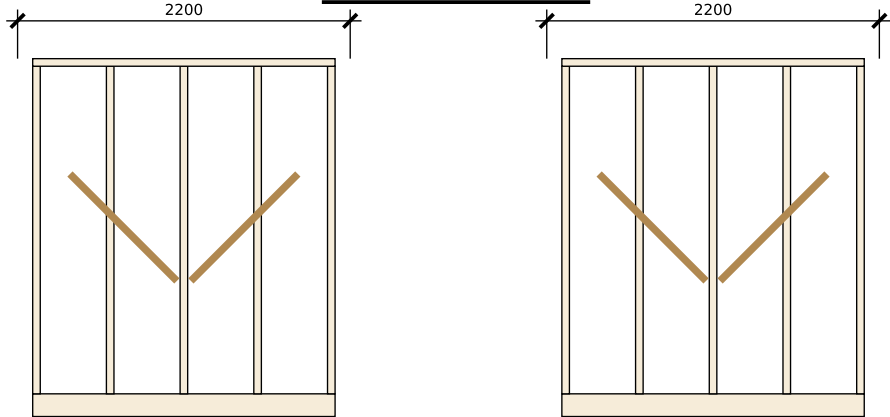


Торцевая стена (ось 1) М 1:50

Торцевая стена (ось 2) М 1:50

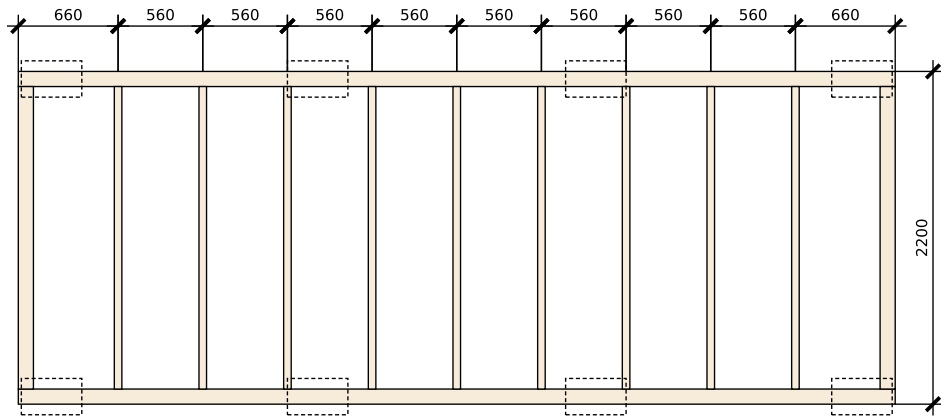

Каркас пола (обвязка, лаги) М 1:50

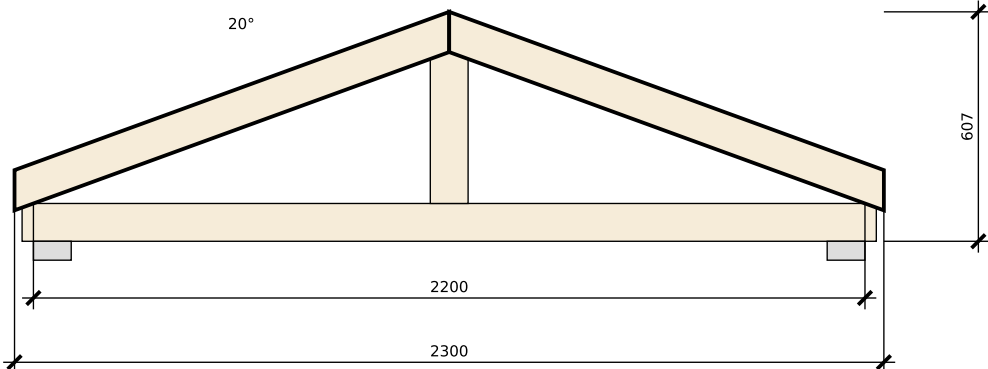


Ферма Ф-1 (11 шт., шаг 575) М 1:20


Спецификация пиломатериала каркаса (без запаса)

Наименование	Сечение	Шт.	Длина, м	Объём, м³
Брус (обвязка)	100×150	4	15.6	0.23
Доска (раскосы, обрешётка)	25×100	18	68.2	0.17
Доска (стойки, фермы)	50×100	87	147.5	0.74
Доска (лаги пола)	50×150	9	18.0	0.14
Итого по каркасу				1.28


Узлы соединения: стойки к обвязке — уголки 90×90 + саморезы 5×50;
фермы к верхней обвязке — уголки 70×70 и косые гвозди 4×100;
лаги к обвязке — опоры бруса 50×150.
Сборку вести в порядке: блоки → обвязка+лаги → черновой пол → стены → фермы → обрешётка/кровля → окна/дверь → утепление → отделка.

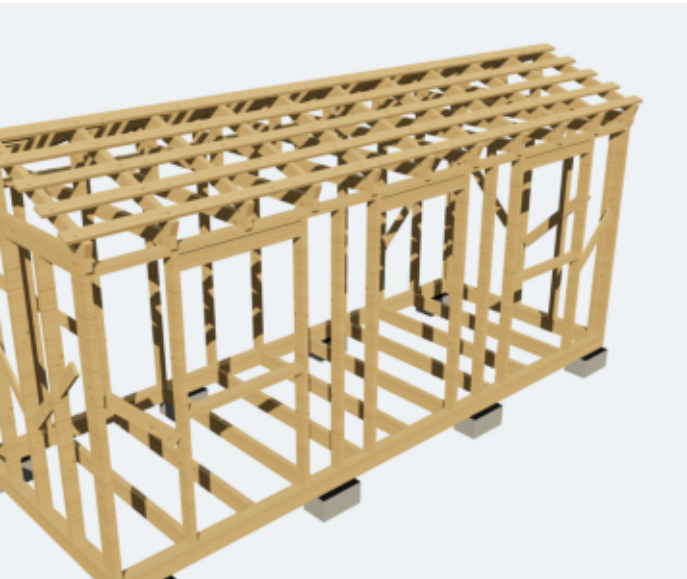

					ХБ-6.0x2.3-AP			
					Хозблок 6,0 × 2,3 м (по крыше) каркасный, утеплённый, с наполнением для хранения	Стадия	Лист	Листов
						Р	5	6
						Частный заказ М 1:50, 1:20		
Изм.	Кор.уч	Лист	Индок.	Подп.	Дата	Каркас. Схемы раскладки элементов	Размеры — мм, отметки — м	
Разраб.			Claude					
Пров.								
Т.контр.								
Н.контр.								
Утв.					09.2026			

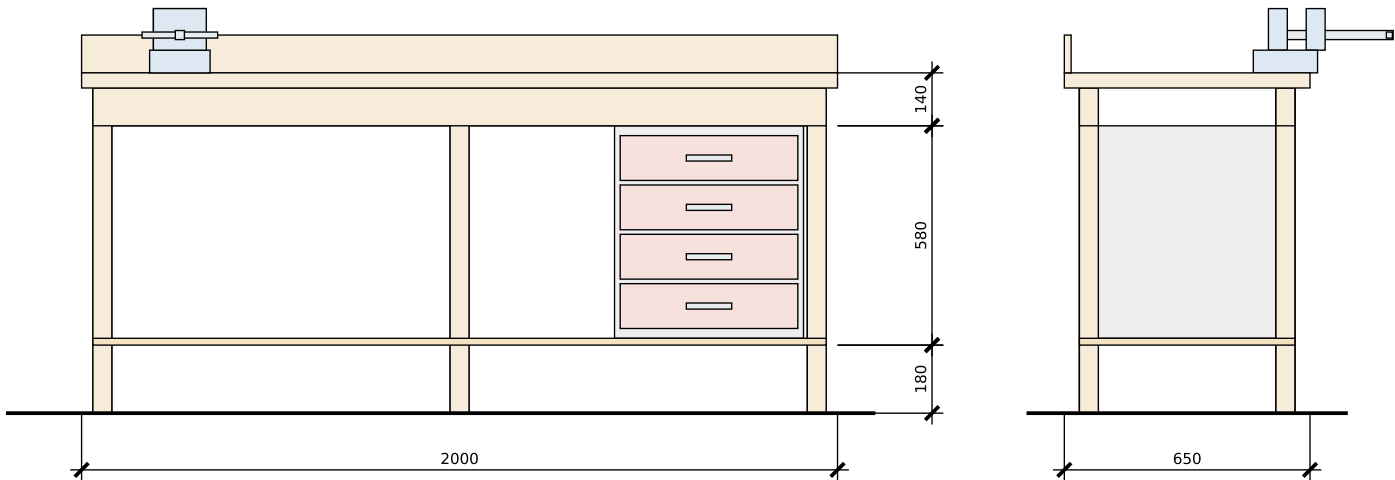


Верстак (поз. 21) — вид спереди М 1:20

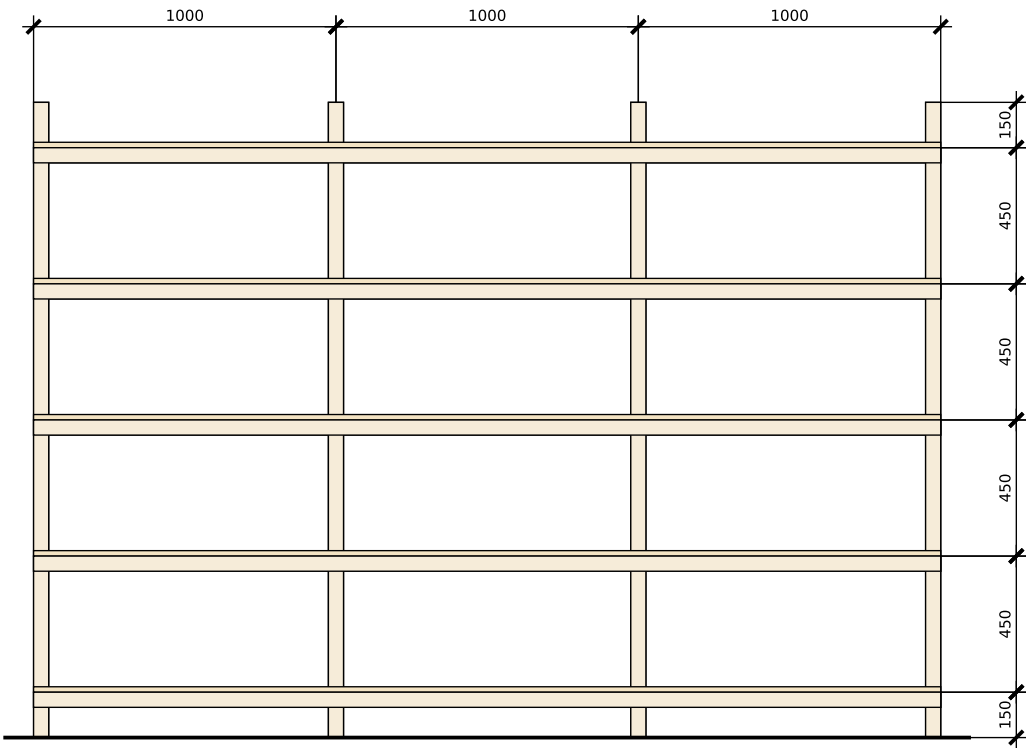

Стеллаж (поз. 25) — фасад М 1:25

Вид сбоку М 1:20

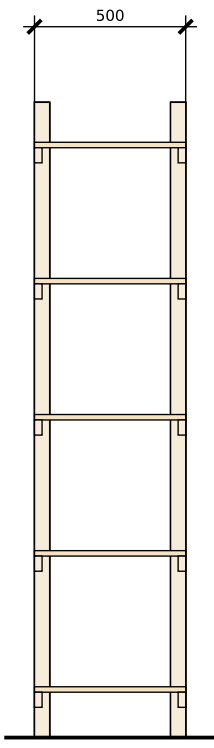


Бок М 1:25

Спецификация материалов наполнения

Поз.	Наименование	Ед.	Кол.
21	Брус 50×100 (ножки, царги)	м	14
21	Фанера ФСФ 18 мм (столешница 2 слоя, борт)	лист	2
21	ОСБ-3 12 мм (нижняя полка)	м²	1,1
22	Тиски слесарные 125 мм + болты М10	шт	1
23	Тумба-кассетница металл., 4 ящика	шт	1
24	Перфопанель стальная 750×1000 + крючки	компл	1
25	Брусок 50×50 (стойки 8×2,1 м)	м	17
25	Брусок 25×50 (царги под полки)	м	30
25,27,28	ОСБ-3 18 мм (полки)	лист	4
26	Доска строганая 25×100 (рейки)	м	5
26	Держатель инструмента настенный	шт	12
27,28	Кронштейн полочный 300/400 мм	шт	9
29	Крюки настенные большие (шланг, удлинитель)	шт	6
33	Коврик резиновый 6 мм	м²	2,9
—	Саморезы, уголки, лак/антисептик	компл	1

- Указания:
- Верстак крепить к стене и полу уголками; столешница — 2 слоя фанеры на клею и саморезах, торец — кромка из доски.
 - Стеллаж крепить к каркасу стены через ОСБ в стойки (саморезы 6×90), нагрузка на полку до 80 кг.
 - Держатели инструмента — на рейки, рейки — в стойки каркаса.
 - Деревянные элементы покрыть антисептиком/лаком.
 - Зона техники у двери — порог-пандус съёмный (опция).

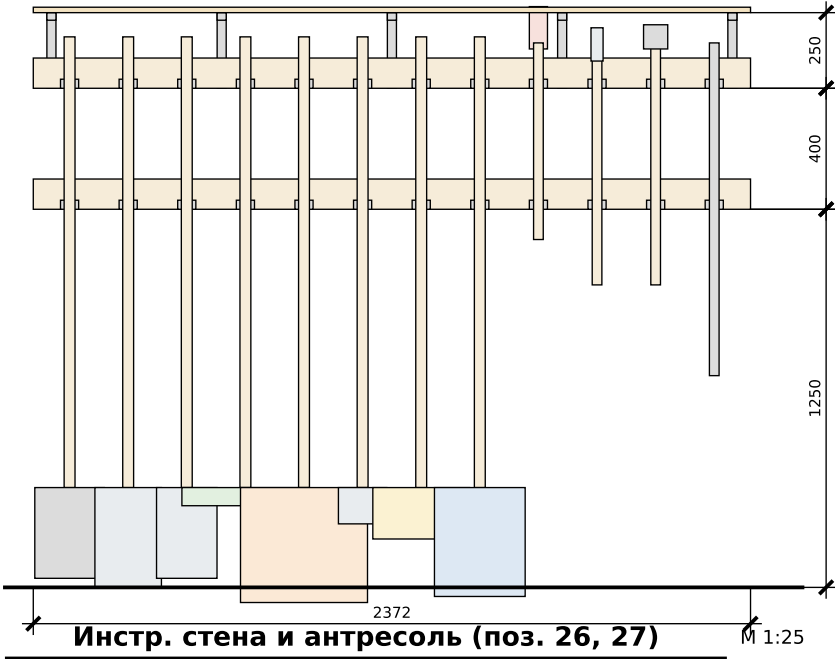

Инстр. стена и антресоль (поз. 26, 27) М 1:25

						ХБ-6.0х2.3-АР			
						Хозблок 6,0 × 2,3 м (по крыше) каркасный, утеплённый, с наполнением для хранения	Стадия	Лист	Листов
							Р	6	6
							Частный заказ М 1:20, 1:25		
Изм.	Кол.уч	Лист	№док.	Подп.	Дата	Оборудование для хранения. Детализовка, спецификация	Размеры — мм, отметки — м		
Разраб.			Claude						
Пров.									
Т.контр.									
Н.контр.									
Утв.					09.2026				